N

CALIRAYA LAKE

(water edge indicative)

ACCESS ROAD

TIMBER JETTY

18.00

DROP-OFF / SERVICE

8 CAR STALLS 2.50 × 5.00

28.50

16.80

6.00

16.00

CALIRAYA COFFEE HOUSE

2 STOREYS · GFA 384 m²

PWD

MC ×6

4 STALLS

SIGN

ENTRANCE

Lot boundary, setbacks and contours to follow topographic survey (not shown).

SCALE 1:500 @ A3

0 10 20 30 40 50 m

CALIRAYA COFFEE HOUSE

Two-storey lakeside café

Caliraya, Lumban–Cavinti, Laguna, Philippines

CONCEPTUAL DESIGN
NOT FOR CONSTRUCTION

NOTES

1. All dimensions in metres unless noted.
2. Dimensions are preliminary design values, not verified site measurements.
3. Levels relative to site datum ±0.00: GF FFL +0.15 · 2F FFL +3.75 · eave +7.15.
4. Verify all dimensions on site. Topographic survey, structural, MEPFS & fire design by licensed professionals required.
5. Plan cut approx. 1.20 m above floor.

LEGEND

- Wall (cut)
- Glazing / window
- Door swing
- Overhead / beyond
- Setting-out grid

AREA SCHEDULE (preliminary)

Ground floor (enclosed)	192.0 m²
Second floor (enclosed)	192.0 m²
Gross floor area	**384.0 m²**
Sunset balcony	33.6 m²
Lakeside deck	90.0 m²
Entrance plaza	88.0 m²
Parking	12 cars + 1 PWD + 6 MC

REV	DATE	DESCRIPTION
A	2026-10-25	Concept issue

SHEET TITLE

SITE PLAN

Building, parking, access & lakeside landscape

SCALE **1:500 @ A3**

DATE **2026-10-25**


DRAWN

CHECKED

SHEET Sheet 1 of 4

A-001

N

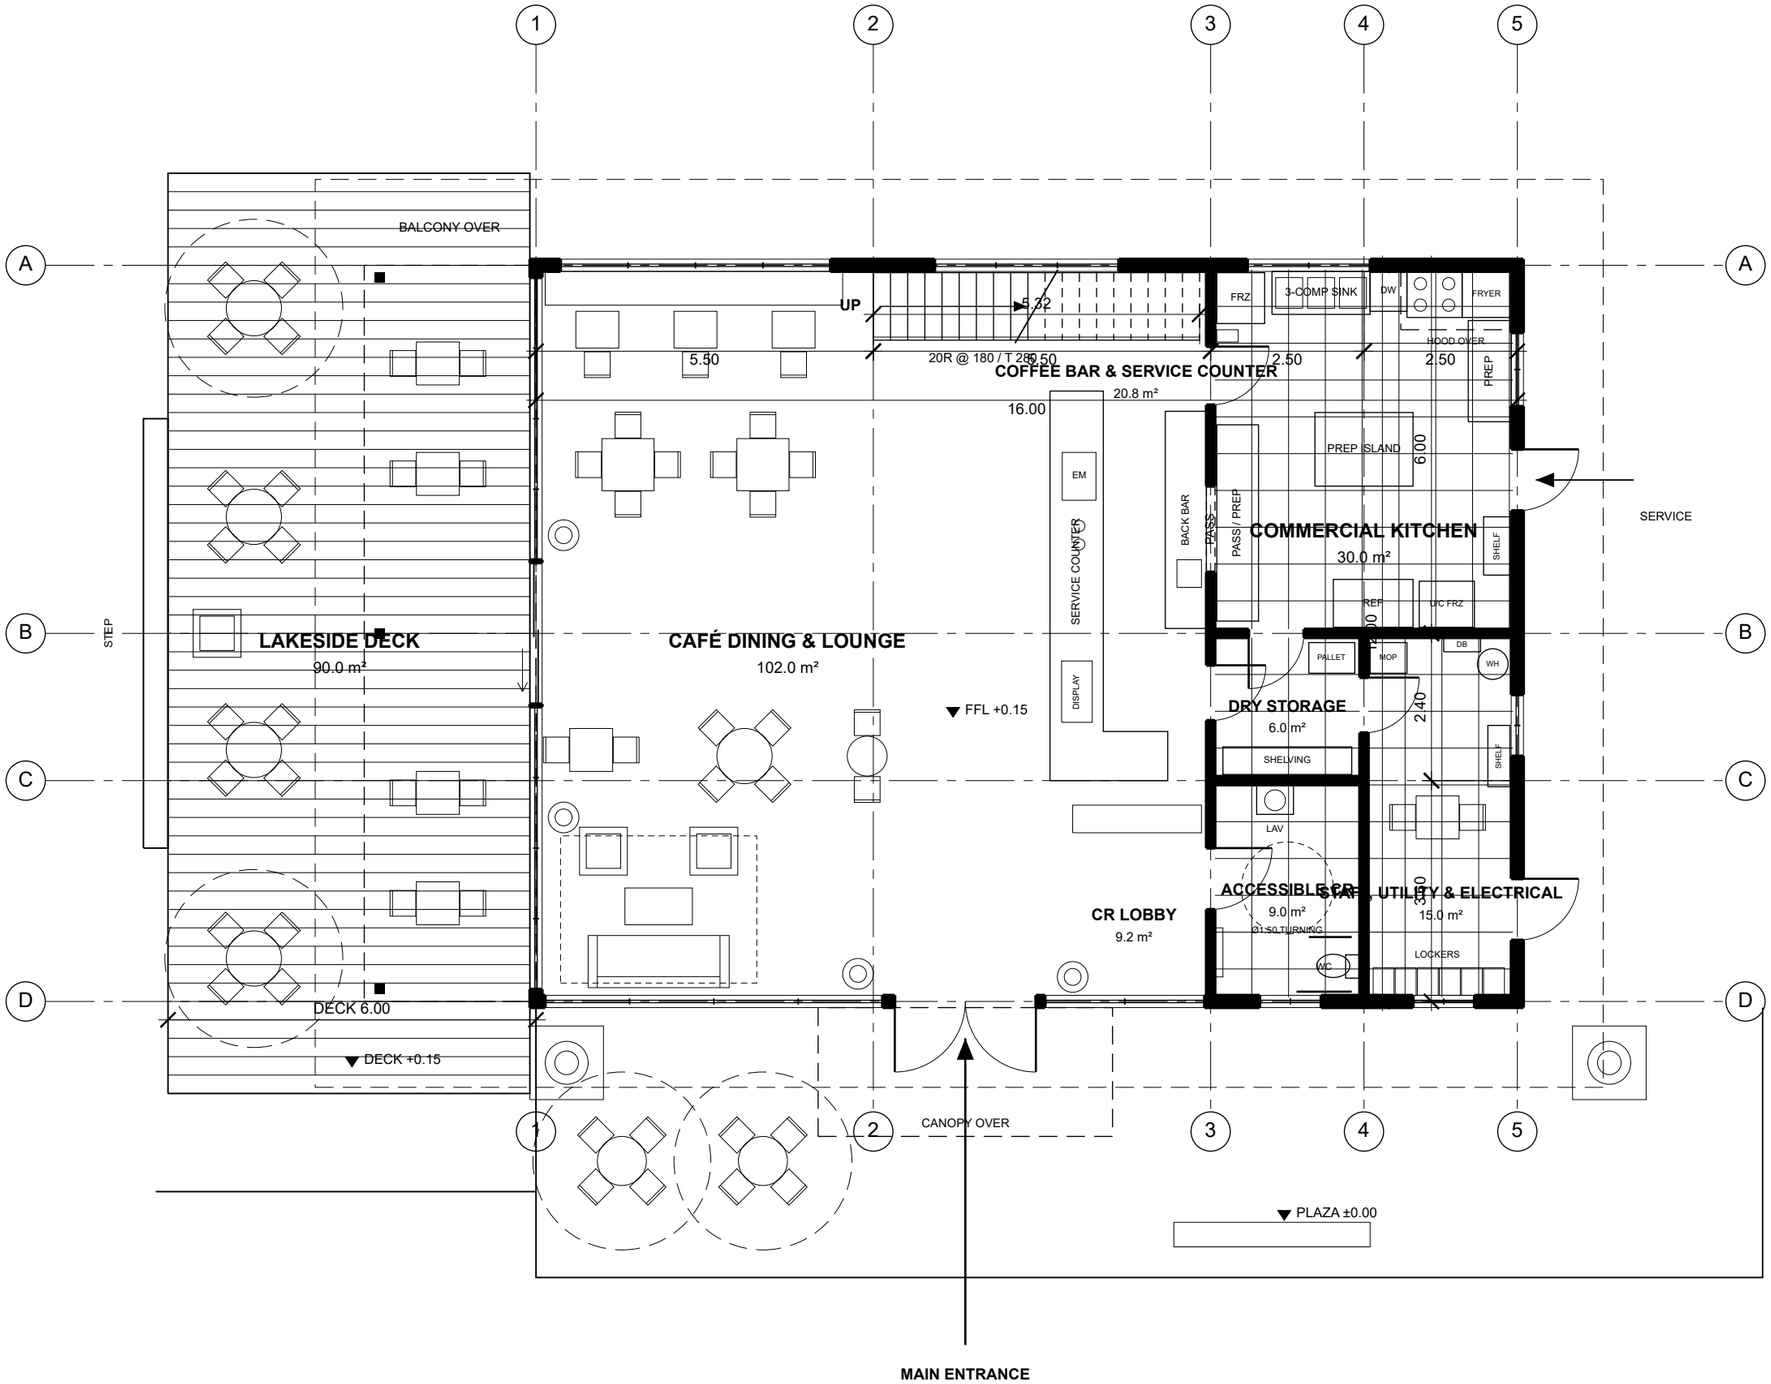

SCALE 1:100 @ A3

0 2 4 6 8 10 m

CALIRAYA COFFEE HOUSE

Two-storey lakeside café

Caliraya, Lumban–Cavinti, Laguna, Philippines

CONCEPTUAL DESIGN
NOT FOR CONSTRUCTION

NOTES

1. All dimensions in metres unless noted.
2. Dimensions are preliminary design values, not verified site measurements.
3. Levels relative to site datum ±0.00: GF FFL +0.15 · 2F FFL +3.75 · eave +7.15.
4. Verify all dimensions on site. Topographic survey, structural, MEPFS & fire design by licensed professionals required.
5. Plan cut approx. 1.20 m above floor.

LEGEND

- Wall (cut)
- Glazing / window
- Door swing
- Overhead / beyond
- Setting-out grid

REV	DATE	DESCRIPTION
A	2026-10-25	Concept issue

SHEET TITLE

GROUND FLOOR PLAN


Café, coffee bar, kitchen, CR & service

SCALE	DATE
1:100 @ A3	2026-10-25
DRAWN	CHECKED

SHEET
Sheet 2 of 4

A-101

N

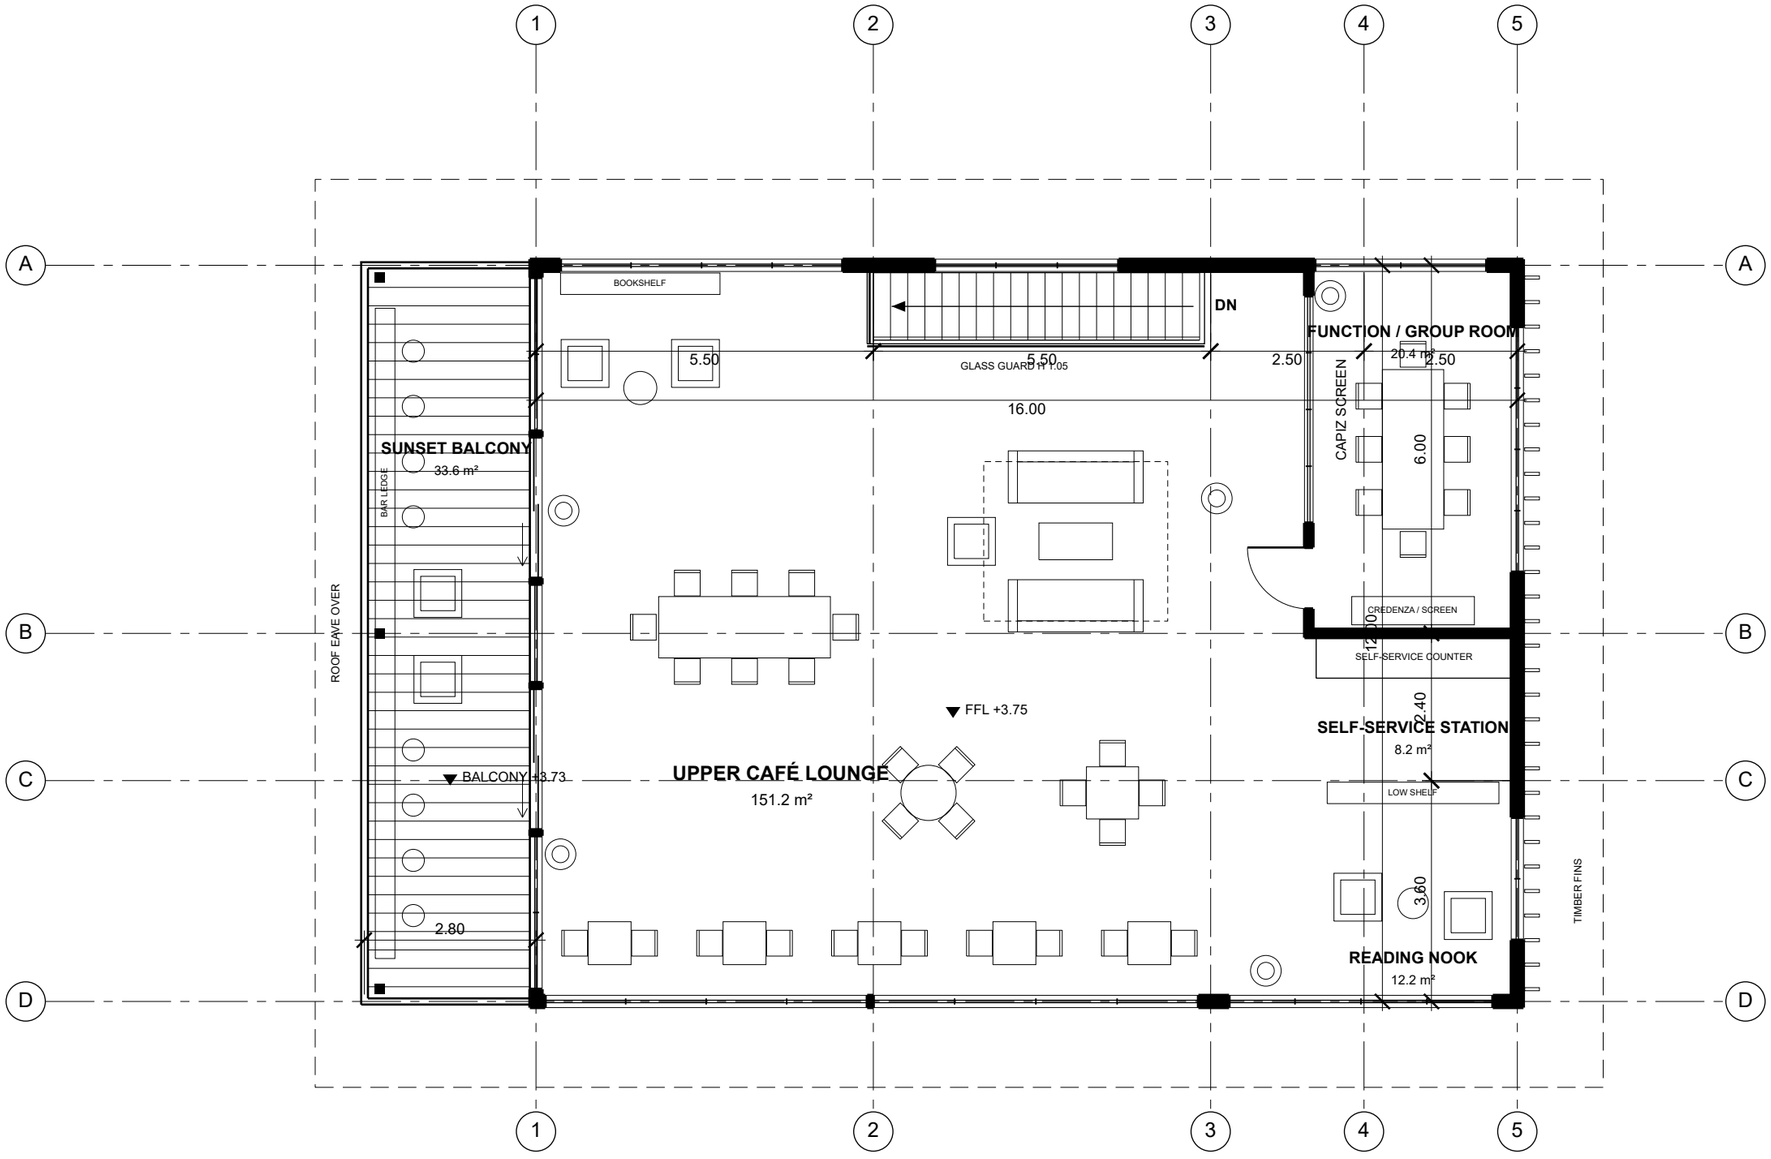

SCALE 1:100 @ A3

0 2 4 6 8 10 m

CALIRAYA COFFEE HOUSE

Two-storey lakeside café

Caliraya, Lumban–Cavinti, Laguna, Philippines

CONCEPTUAL DESIGN
NOT FOR CONSTRUCTION

NOTES

1. All dimensions in metres unless noted.
2. Dimensions are preliminary design values, not verified site measurements.
3. Levels relative to site datum ±0.00: GF FFL +0.15 · 2F FFL +3.75 · eave +7.15.
4. Verify all dimensions on site. Topographic survey, structural, MEPFS & fire design by licensed professionals required.
5. Plan cut approx. 1.20 m above floor.

LEGEND

- Wall (cut)
- Glazing / window
- Door swing
- Overhead / beyond
- Setting-out grid

REV	DATE	DESCRIPTION
A	2026-10-25	Concept issue

SHEET TITLE

SECOND FLOOR PLAN


Upper lounge, function room & sunset balcony

SCALE	DATE
1:100 @ A3	2026-10-25
DRAWN	CHECKED

SHEET
Sheet 3 of 4

A-102

N

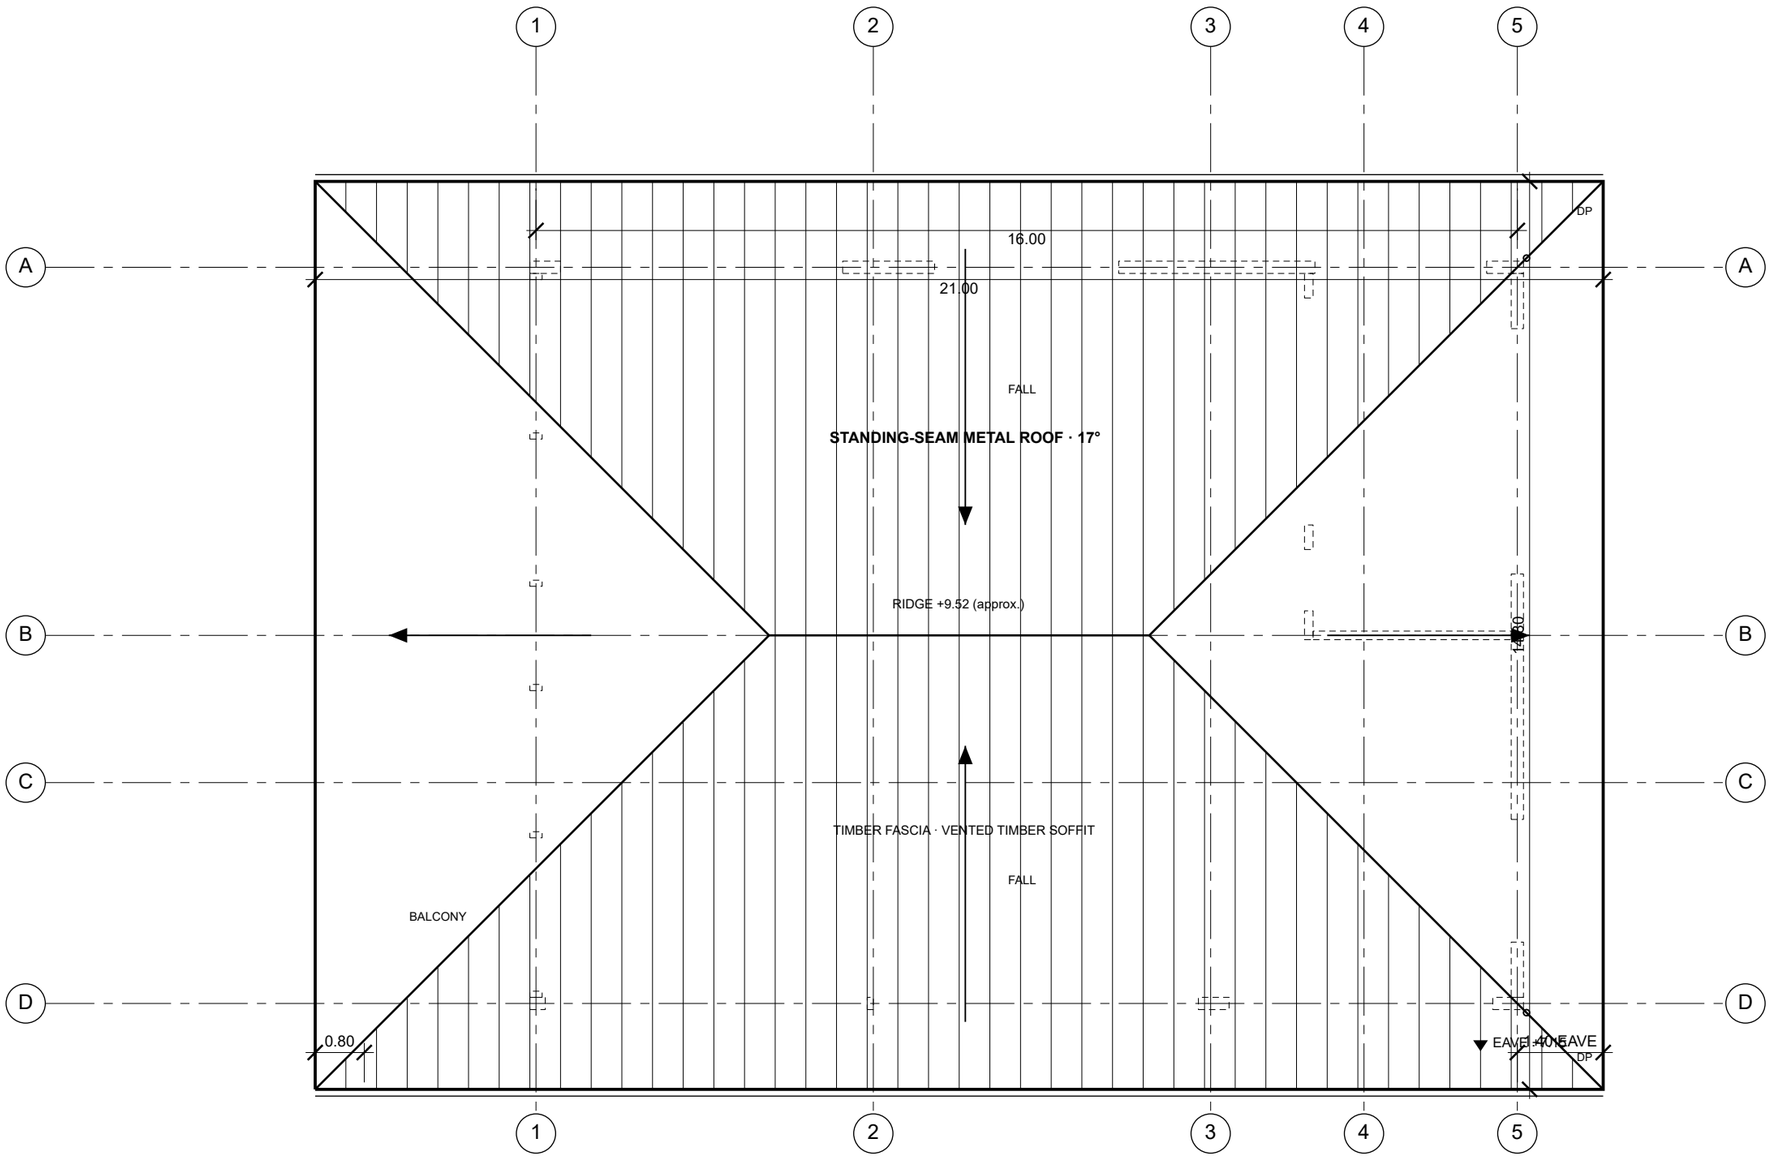

SCALE 1:100 @ A3

0 2 4 6 8 10 m

CALIRAYA COFFEE HOUSE

Two-storey lakeside café

Caliraya, Lumban–Cavinti, Laguna, Philippines

CONCEPTUAL DESIGN
NOT FOR CONSTRUCTION

NOTES

1. All dimensions in metres unless noted.
2. Dimensions are preliminary design values, not verified site measurements.
3. Levels relative to site datum ±0.00: GF FFL +0.15 · 2F FFL +3.75 · eave +7.15.
4. Verify all dimensions on site. Topographic survey, structural, MEPFS & fire design by licensed professionals required.
5. Plan cut approx. 1.20 m above floor.

LEGEND

- Wall (cut)
- Glazing / window
- Door swing
- Overhead / beyond
- Setting-out grid

REV	DATE	DESCRIPTION
A	2026-10-25	Concept issue

SHEET TITLE

ROOF PLAN

Hip roof, standing-seam metal, 17° pitch

SCALE	DATE
1:100 @ A3	2026-10-25
DRAWN	CHECKED

SHEET
Sheet 4 of 4

A-103